
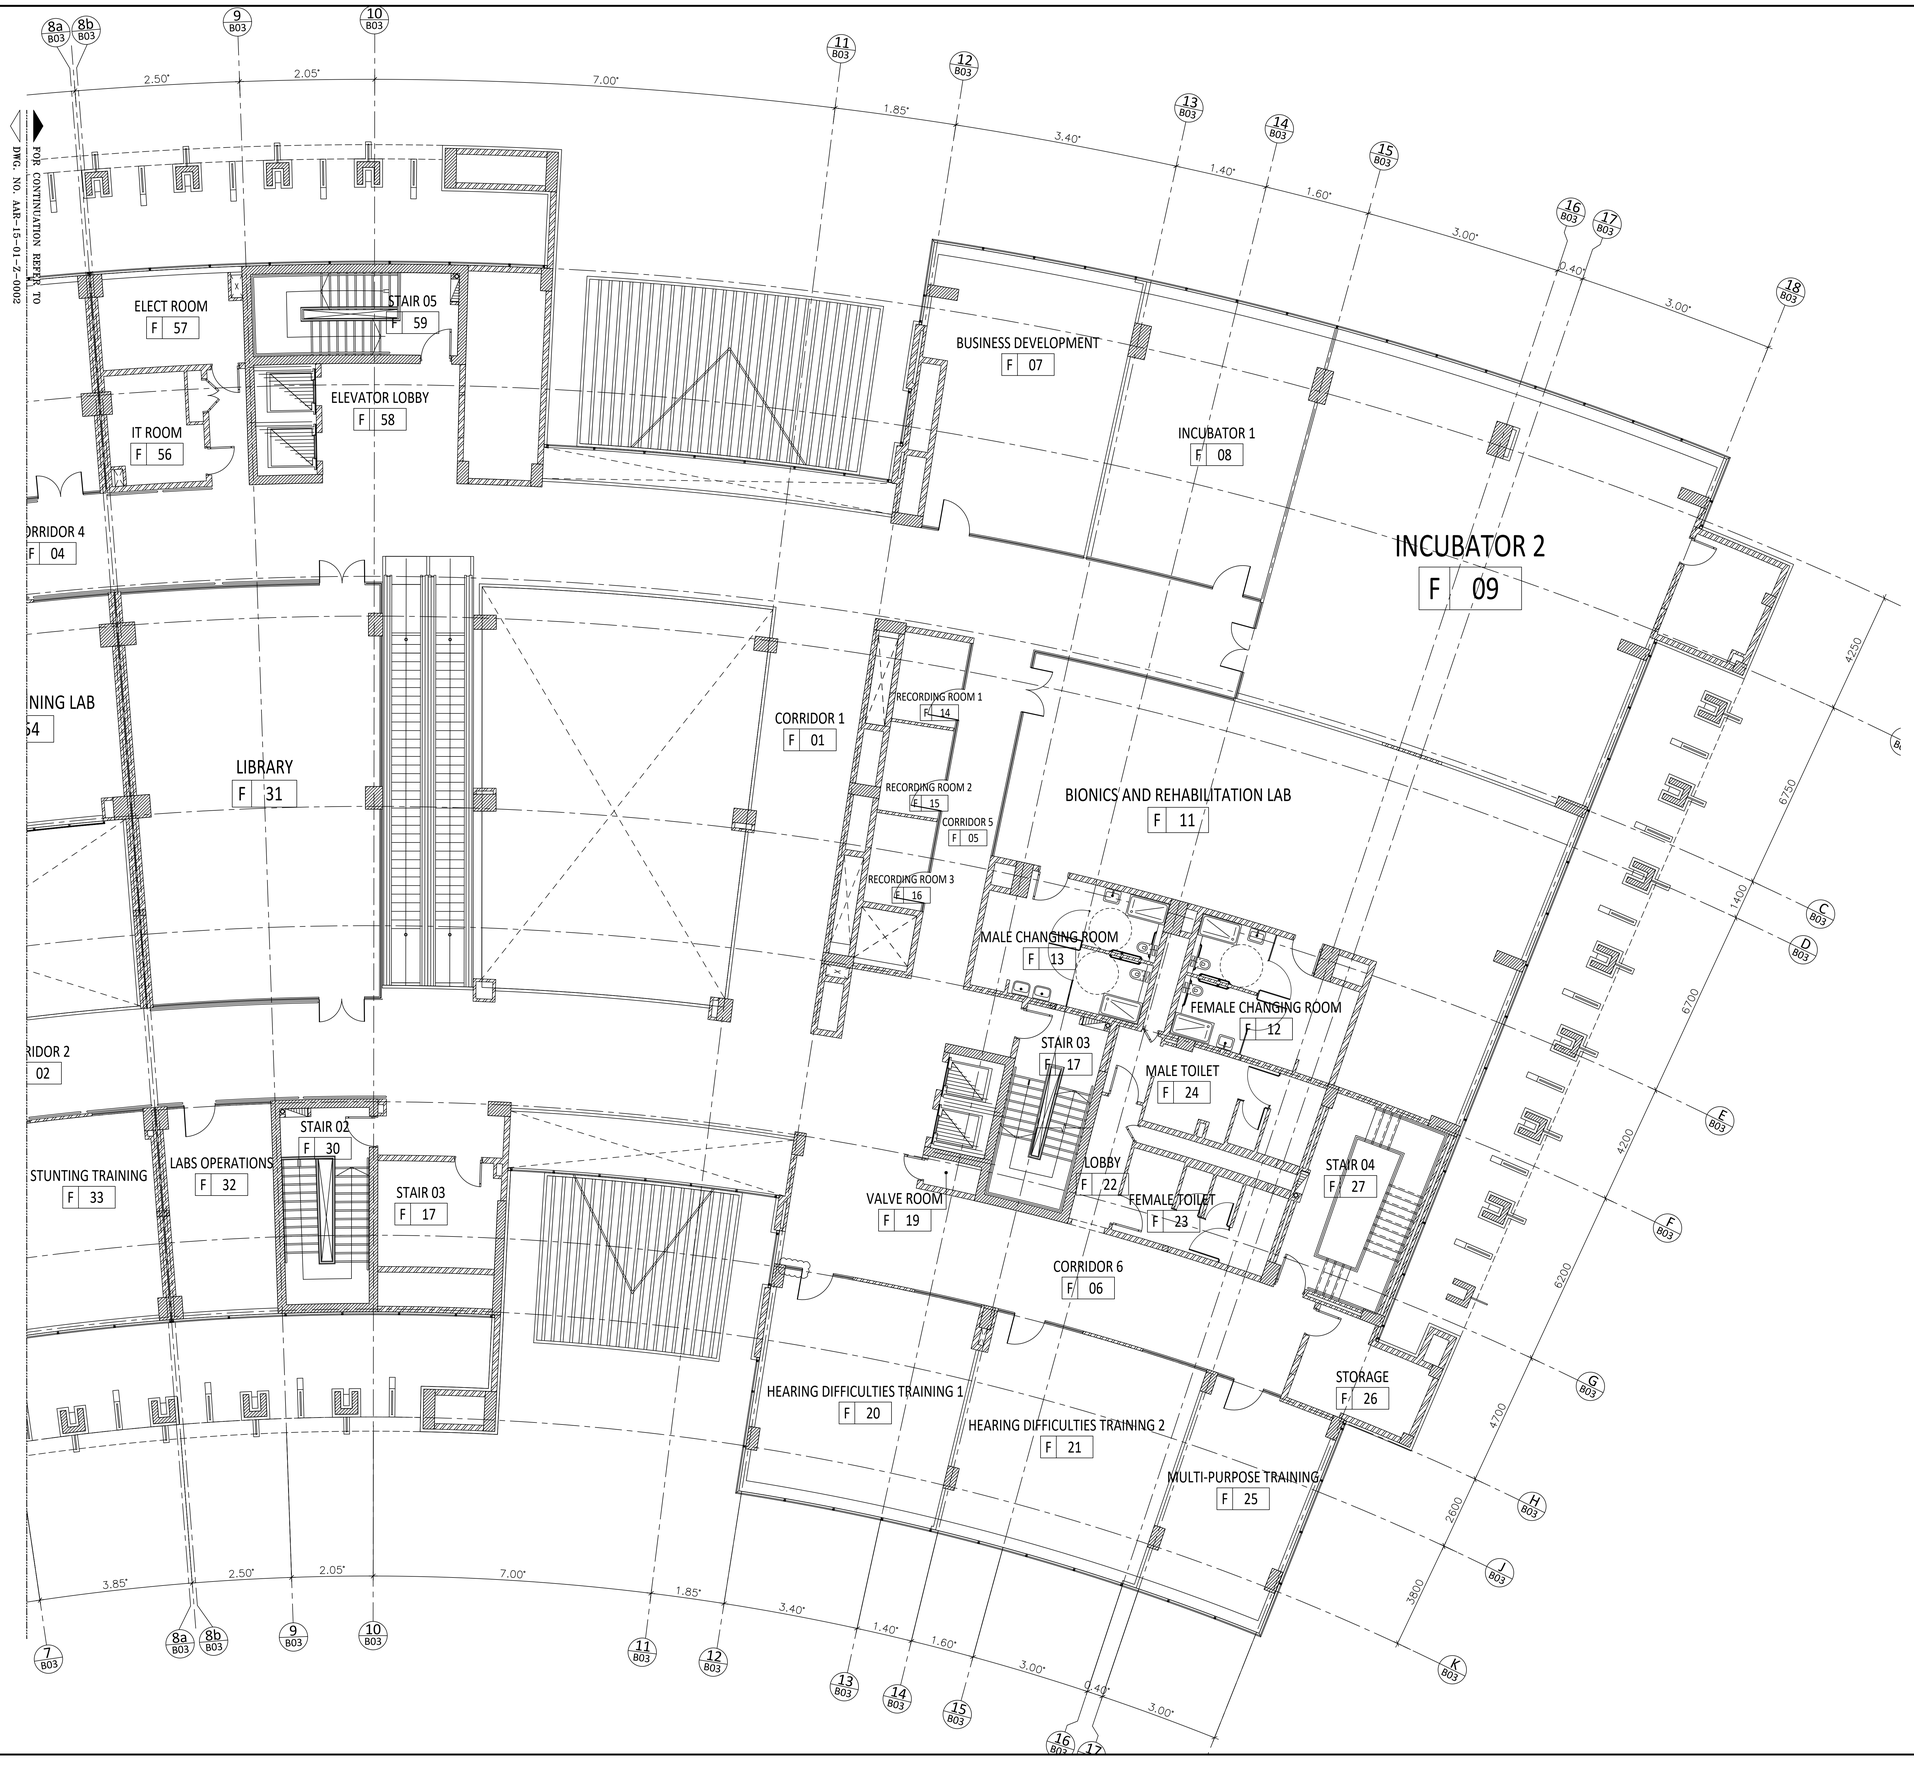


REFERENCE DRAWINGS	DWG NO.	REV
ARCHITECTURE DESIGN	AE-103M	02
STRUCTURE	B03-SF103P	02
SITE ORDER	NUMBER 57	00
RFI	SOD-ECG-RFI-ARCH-0445	00

GENERAL NOTES :

Project KeyPlan:

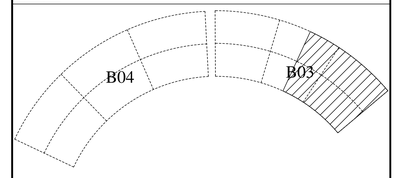

COORDINATION :

	ARCH.	ARCH. SLAB EDGE	STRUCT.	ELECT.	MECH.
DWG.					
DOC.					
DATE					
SIGN.					

NO.	REVISIONS	DATE	DRA.	M.M.	M.M.	ENG.	Y.A. CHK.
00	ISSUED FOR APPROVAL	22/12/2021					

PROJECT : مشروع

KNOWLEDGE CITY
BLOCK B3 & B4

MAIN CONTRACTOR : المقاول العام

وزارة الدفاع
الهيئة الهندسية للقوات المسلحة

CLIENT : المالك

Arab Republic of Egypt
Ministry of Communications and Information Technology

ADMINISTRATIVE CAPITAL FOR URBAN DEVELOPMENT

CONSULTANT : الاستشاري

استشاري الهيئة الهندسية للتصميم المعماري والانشاء
ECG
ENGINEERING CONSULTANTS GROUP S.A.
www.ecgsa.com

CONTRACTOR : المقاول

السعداء جروب للتشييد والبناء
ش.م.م

El Soadaa Group

Type of document :

SHOP DRAWING

Drawing title :

SIGNAGE & SPACES NUMBERS LAYOUT
FIRST FLOOR(B03) - PART 02

Drawn by		Checked by		Approved by	

Drawing No.	Project No.	Company	Building Type	Document Type	Sub Trade	Element Type	Floor Level	Zone No.	Sheet No.	Revision No.	Scale	Date
	2761	SOD	B03	DWG	AAR	15	01	Z	0002	00	-	22/12/2021