

GROUND FLOOR	
CODE	ROOM NAME
G-01	MAIN ENTRANCE
G-02	CORRIDOR 1
G-03	CORRIDOR 2
G-04	CORRIDOR 3
G-05	AUDITORIUM
G-06	STORAGE
G-07	VIP SALON
G-08	STAIRS 3
G-09	ELEVATOR LOBBY
G-10	VALVE ROOM
G-11	STORAGE
G-12	FEMALE TOILETS
G-13	MALE TOILETS
G-14	LOBBY
G-15	TRANSLATION ROOM
G-16	AUDIO VISUAL
G-17	STAIRS 4
G-18	CAFETERIA
G-19	SERVICE
G-20	KITCHEN
G-21	STORAGE
G-22	SECURITY ROOM
G-23	STAIR 02
G-24	EXHIBITION ROOM
G-25	OPERATIONS OFFICE
G-26	SKYLIGHT
G-27	RECEPTION
G-28	CLINIC
G-29	LOUNGE
G-30	MEETING ROOM
G-31	LOBBY
G-32	STAIRS 1
G-33	PRAYER ROOM
G-34	STORAGE
G-35	COPY ROOM
G-36	ARCHIVES ROOM
G-37	GARBAGE CHUTE
G-38	CONTROL ROOM
G-39	SERVICES
G-40	STORAGE
G-41	FEMALE TOILET
G-42	MALE TOILET
G-43	MECHANICAL LAB
G-44	AV CONTROL ROOM
G-45	PHYSICAL TRAINING LAB 1
G-46	PHYSICAL TRAINING LAB 2
G-47	AV STUDIO
G-48	SERVICE ROOM
G-49	HVAC CABINET
G-50	VISUAL TRAINING LAB 1
G-51	IT ROOM
G-52	ELECT ROOM
G-53	ELEVATOR LOBBY
G-54	STAIRS 5

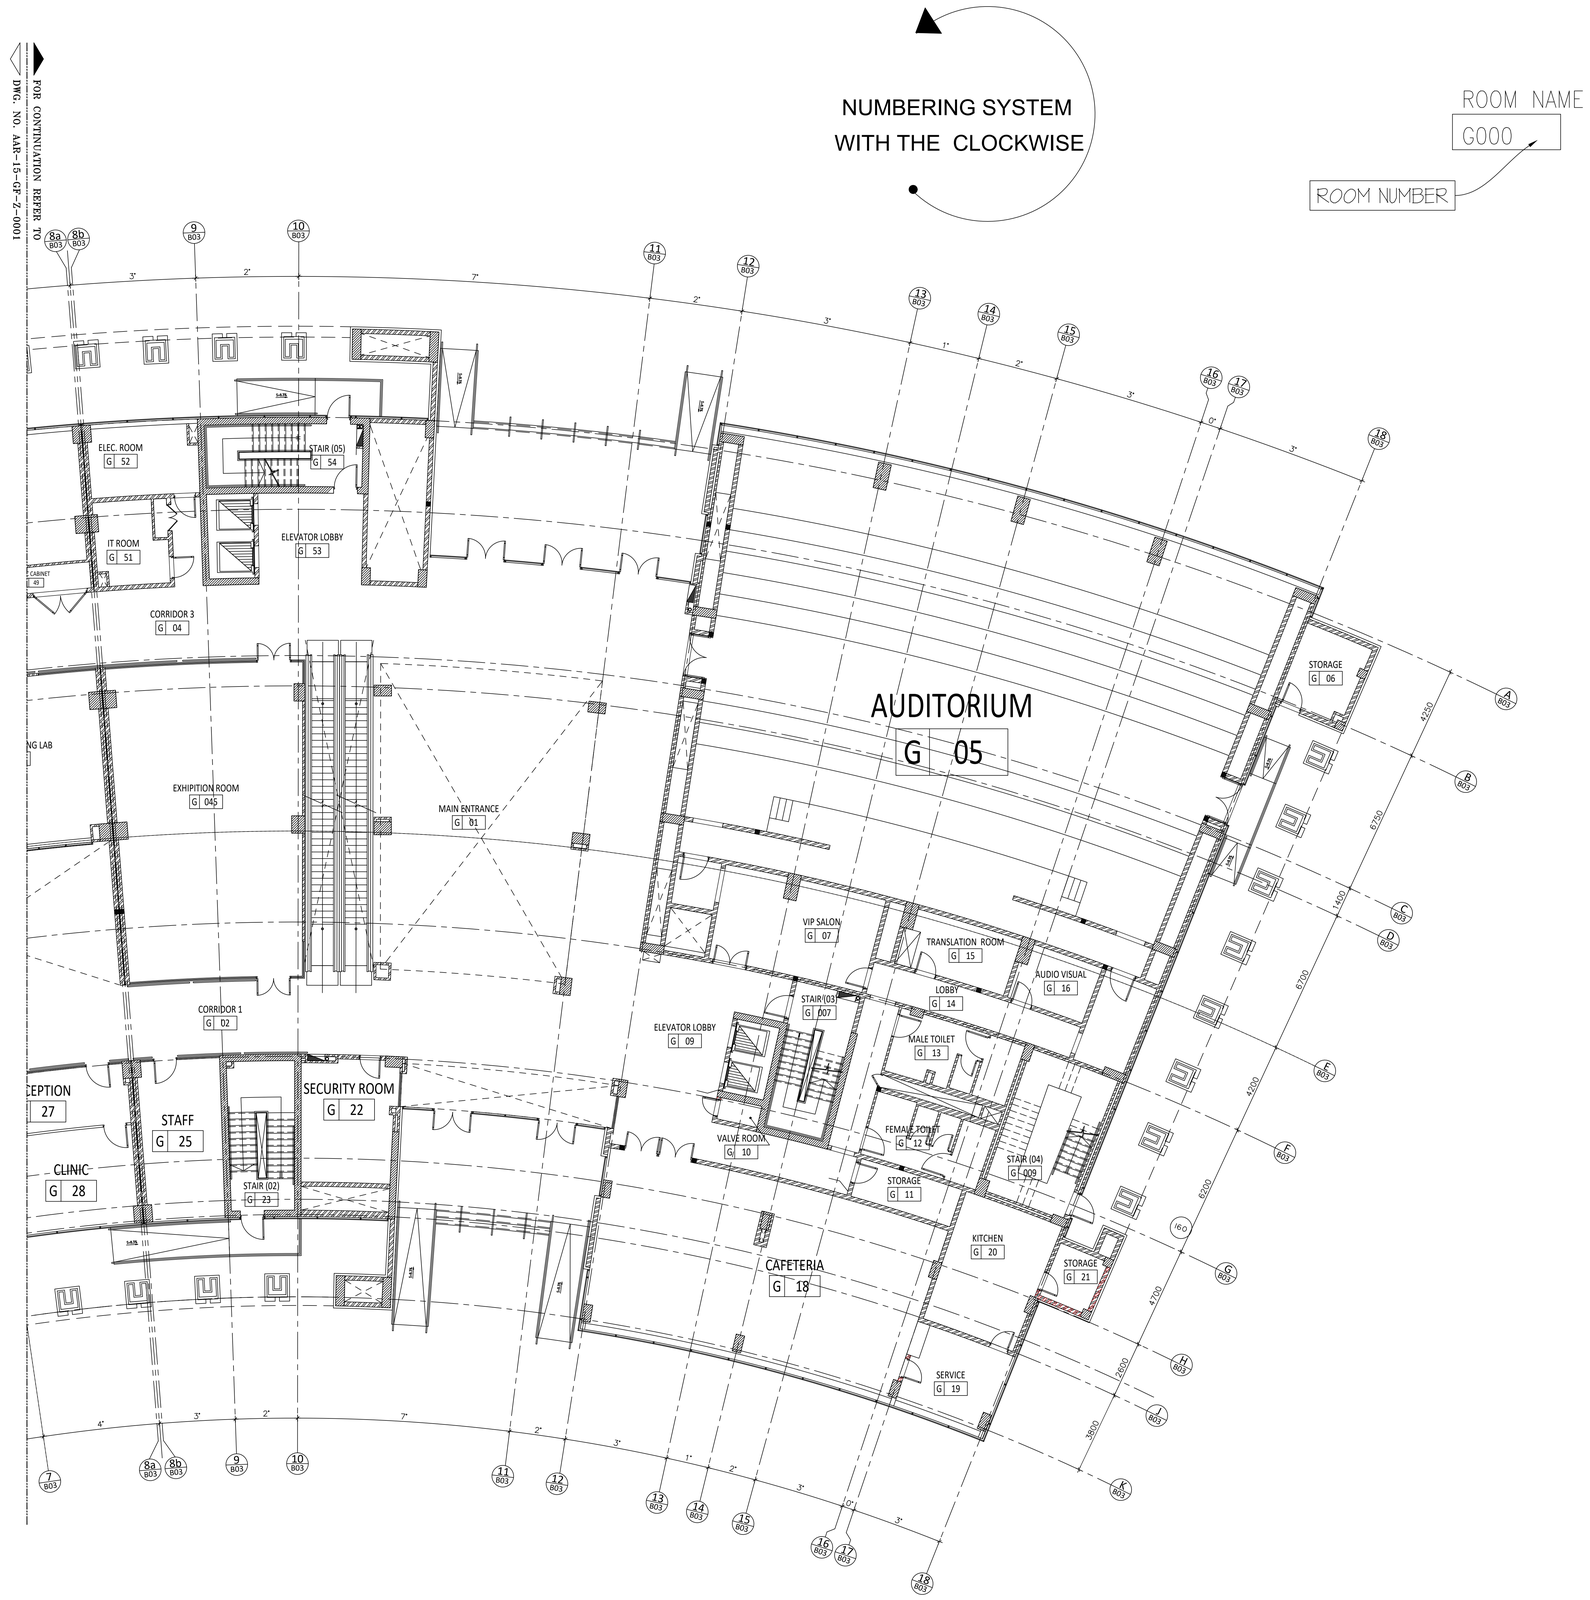

REFERENCE DRAWINGS	DWG NO.	REV
ARCHITECTURE DESIGN	AE-1102M	01
SHOP DRAWING STUC.	2761-SOD-B03-DWG-SSC-02-GF-ZZ-00	00
SHOP DRAWING ARCH.	2761-SOD-GN-DWG-AAR-06-ML-Z-0001	00
RFI	SOD-ECG-RFI-ARCH-0445	00

GENERAL NOTES :

Project KeyPlan:

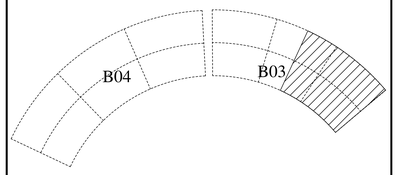

COORDINATION :

	ARCH.		STRUCT.	ELECT.	MECH.
	ARCH.	SLAB EDGE			
DWG.					
DOC.					
DATE					
SIGN.					

NO.	REVISIONS	DATE	DRA.	ENG.	CHK.
01	ISSUED FOR APPROVAL	22/12/2021	M.M.	M.M.	Y.A.
00	ISSUED FOR APPROVAL	07/10/2021	M.M.	M.M.	Y.A.

PROJECT : مشروع

KNOWLEDGE CITY
BLOCK B3 & B4

MAIN CONTRACTOR : المقاول العام

وزارة الدفاع
الهيئة الهندسية للقوات المسلحة

CLIENT : المالك

Arab Republic of Egypt
Ministry of Communications and Information Technology

ADMINISTRATIVE CAPITAL FOR URBAN DEVELOPMENT

CONSULTANT : الاستشاري

استشاري الهيئة الهندسية للتصميم المعماري والانشائي
ECG
ENGINEERING CONSULTANTS GROUP S.A.E.
www.ecgka.com

CONTRACTOR : المقاول

السعداء جروب للتشييد والبناء
ش.م.م

El Soadaa Group

Type of document : SHOP DRAWING

Drawing title :

SIGNAGE & SPACES NUMBERS LAYOUT
@ GROUND FLOOR (B03) - PART 2

Drawn by		Checked by		Approved by	

Drawing No.

Project No.	Company	Building Type	Document Type	Sub Trade	Element Type	Floor Level	Zone No.	Sheet No.	Revision No.	Scale	Date
2761	SOD	B03	DWG	AAR	15	GF	Z	0002	01	--	22/12/2021